


1 Section Facing Hala Holopeka
Scale: 3/16" = 1'-0"

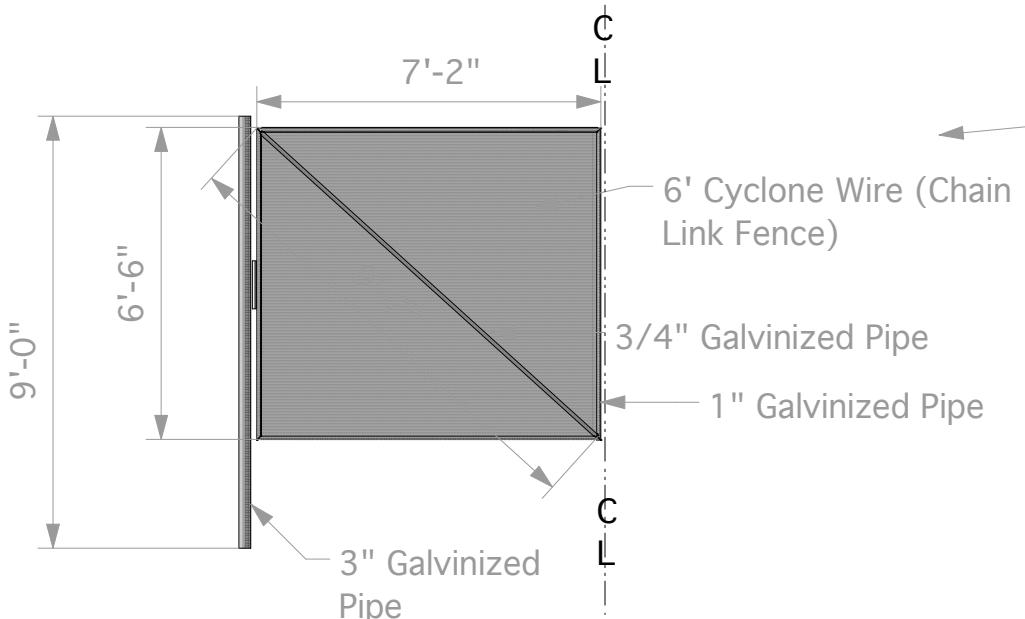

2 Gate Detail
Scale: 1/4" = 1'-0"

General Notes

1. The gate doors will be constructed out of galvanized pipe with cyclone wire drawn across. There will be a cross brace inside of the doors, to support the weight. The hinges will be constructed out of pipe. With 3/4" interior pivoting inside a 1" pipe. The hinge will be 12" long. The doors will swing open, and be chained shut to prevent animal and human tampering.

Contact Number: (676) 60400 Mobile: (676) 3781858	Organization: Ministry of Agriculture, Forestry and Food Ha'apai, Kingdom of Tonga South Pacific
Project Manager: Director of MAFFF Ha'apai	Version Number: Version 2.0
Drawn By: Alyssa Lapan PCV	Sheet Scale:
Designed By: Sunia Napa'a	Drawing Title Section Facing Road
Date: September 13, 2010	Project Name: MAFFF Ha'apai Nursery Project
CAD File Name: MAFFF_ShadeGarden	
Drawing No. 4 of 4 Total Sheets	

